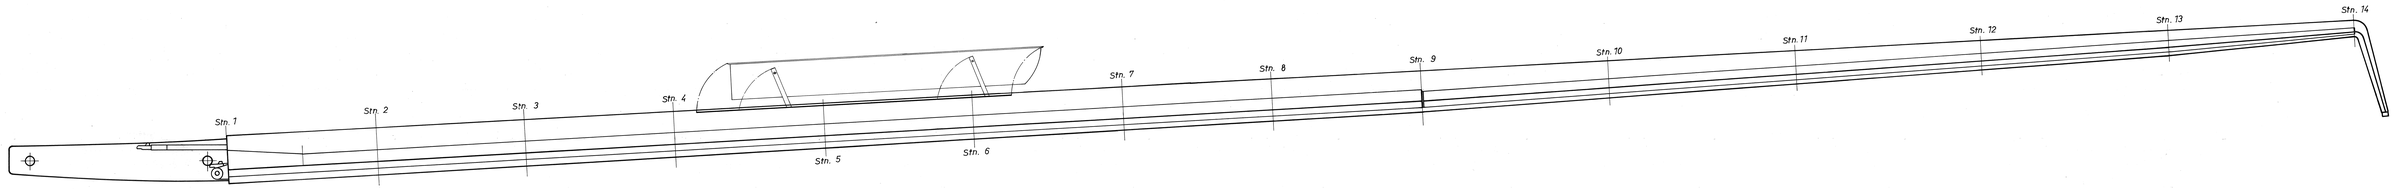

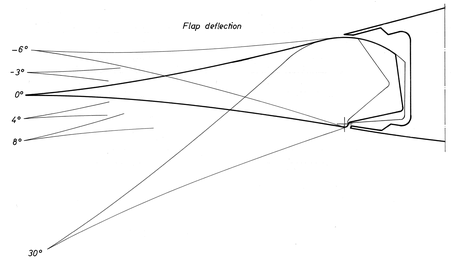

Flap	α_1	α_2
-6°	-40°	14°
-3°	-34°	16°
0°	-30°	18°
4°	-25°	20°
8°	-24°	20°
30°	-42°	13°

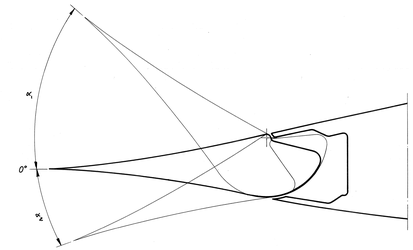

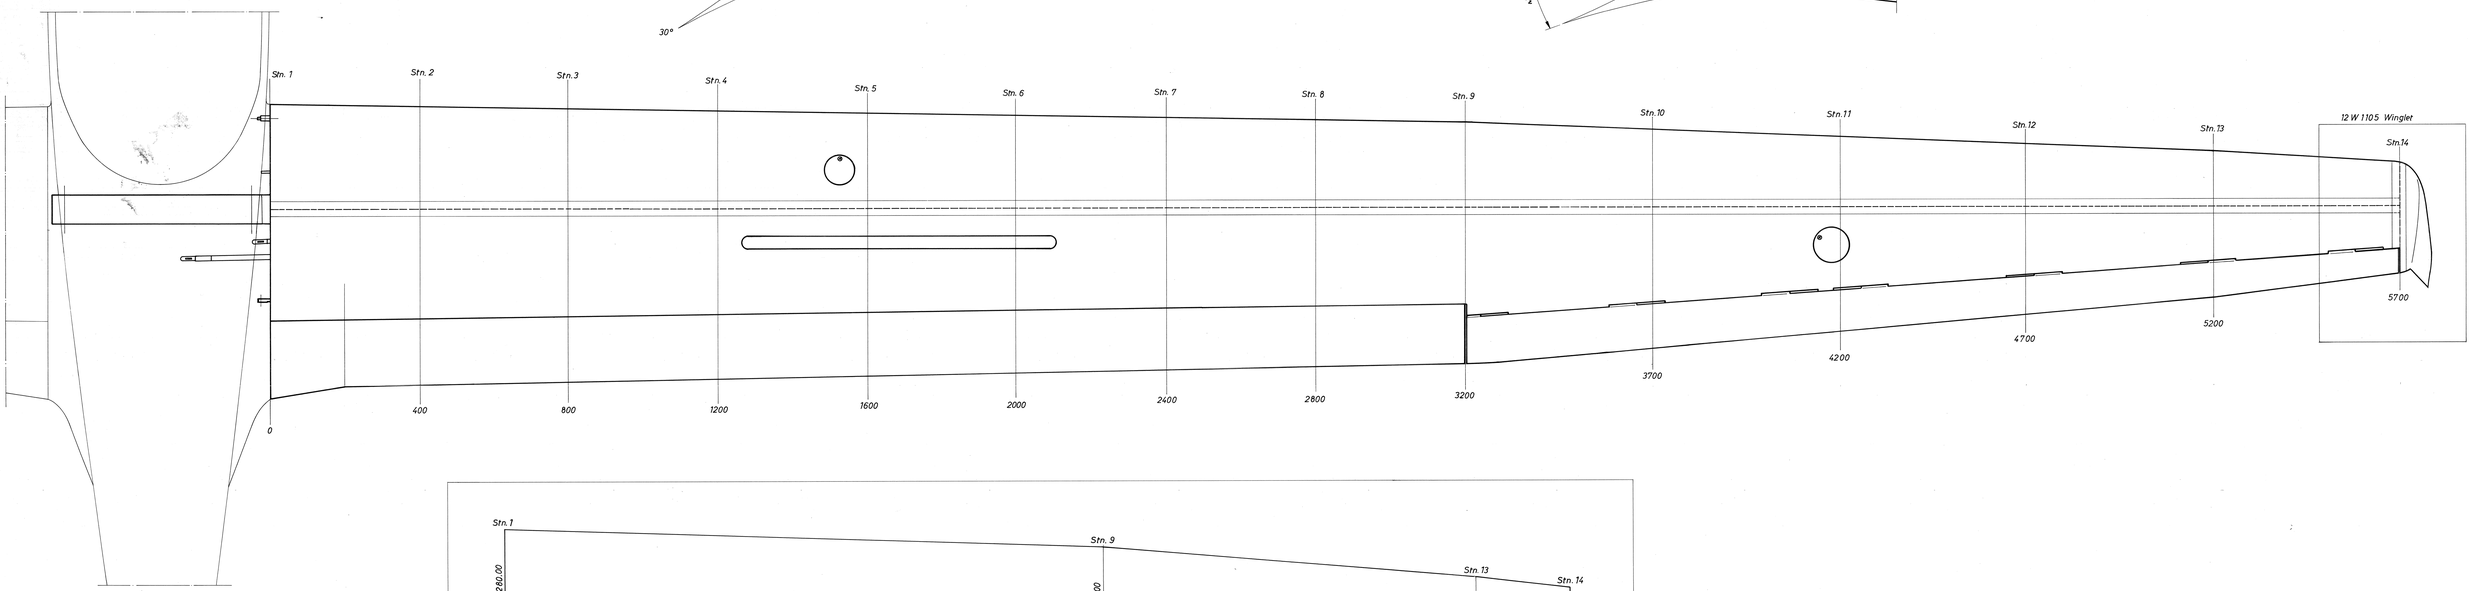

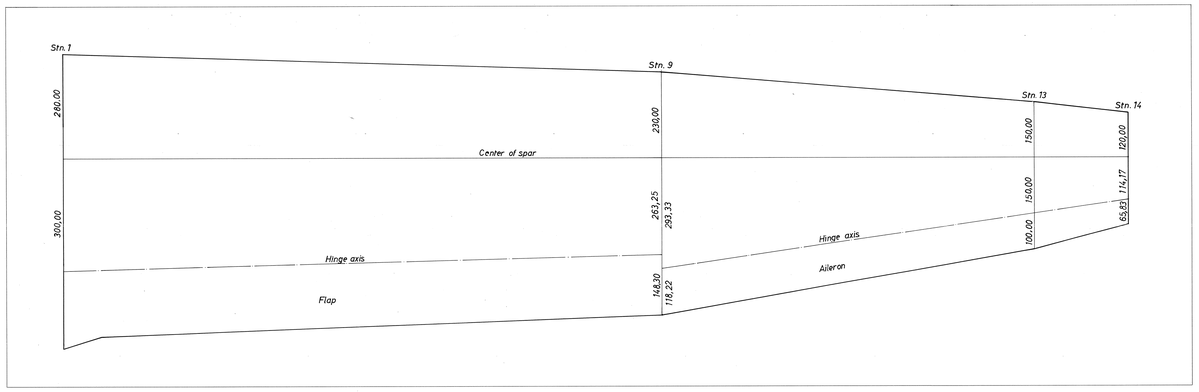

Drawing not to scale

Stn. 1 - 14 on page 2 - 15.

Det. nr / Pos. no	Ant. / Qty.	Benämning / Denomination	Material	Mod. no Ämne Matl. / Dimension	Anmärkning / Remarks
Konstr. / Constr.		Ritad / Drawn: BJAT Kontr. / Contr.	Godk. / Approved	Skala / Scale	Ersätter / Replaces Ersatt av / Replaced by
WINDEX 1200 RADAB AB STOCKHOLM, SWEDEN		WING			Rev. nr / Drawing No 12 W 1100 1 of 15

Ex Pkt 4829/4 Riktlinjekonstruktion 1974/4 mb. 1979/0